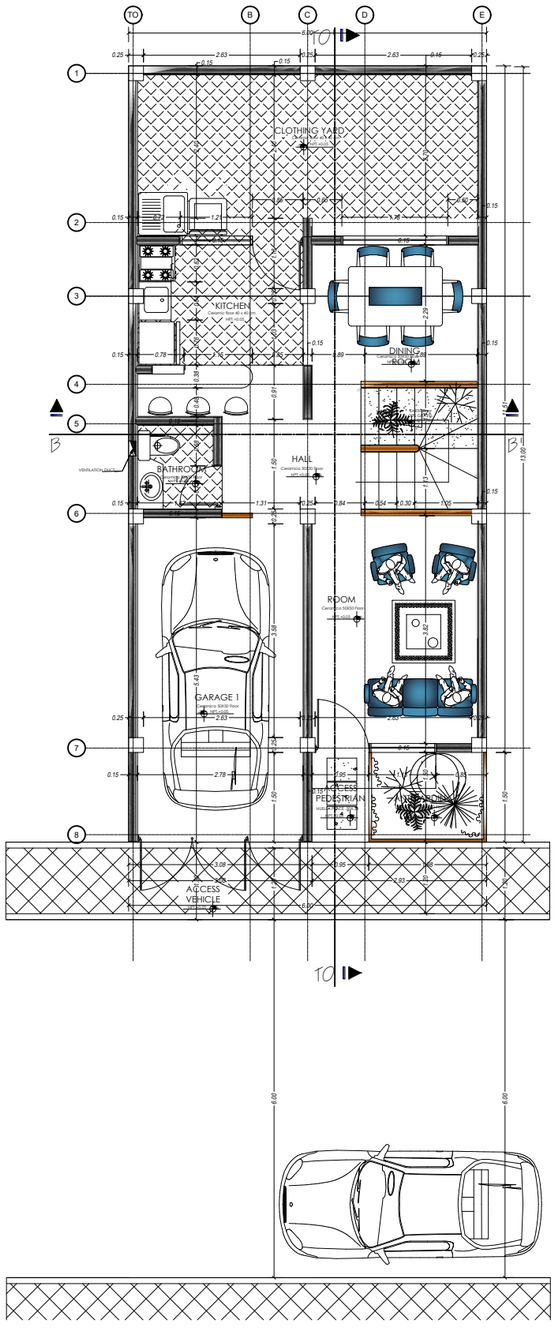

FIRST FLOOR FLOOR

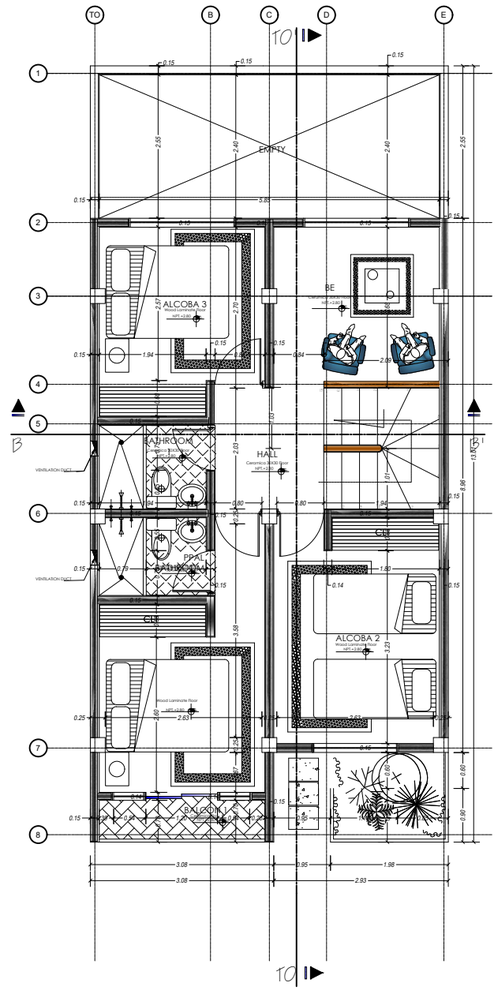

SECOND FLOOR FLOOR

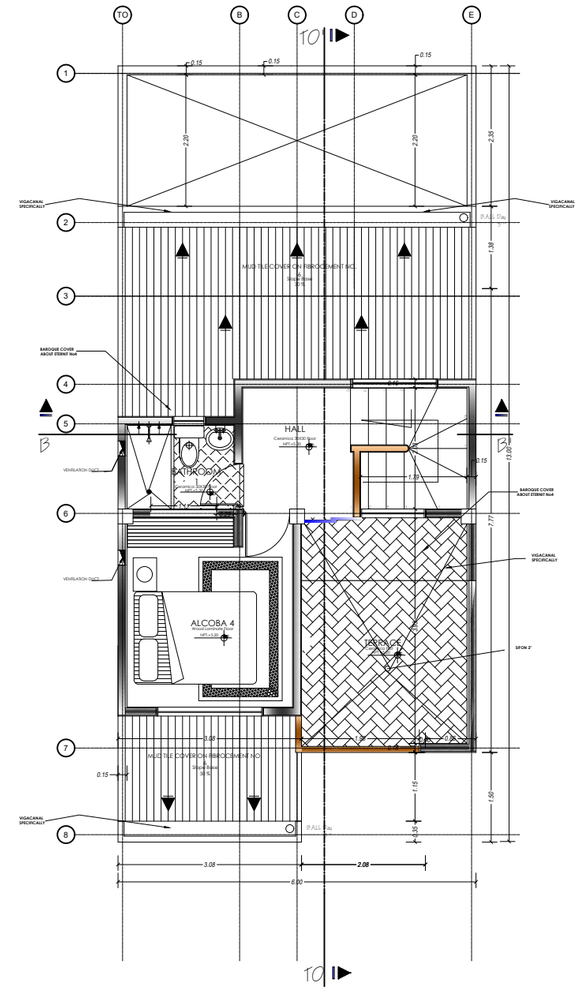

MEZZANINE FLOOR

For more plans like these visit:

freecadfloorplans.com

Project name:	20X40 house 4 bedroom
Drawing title:	Architectural plans
CAD drawing:	-
Scale	1:100
Sheet number	01

This plans are for educational or personal use only, it is illegal by copyright laws to use it for commercial purposes.

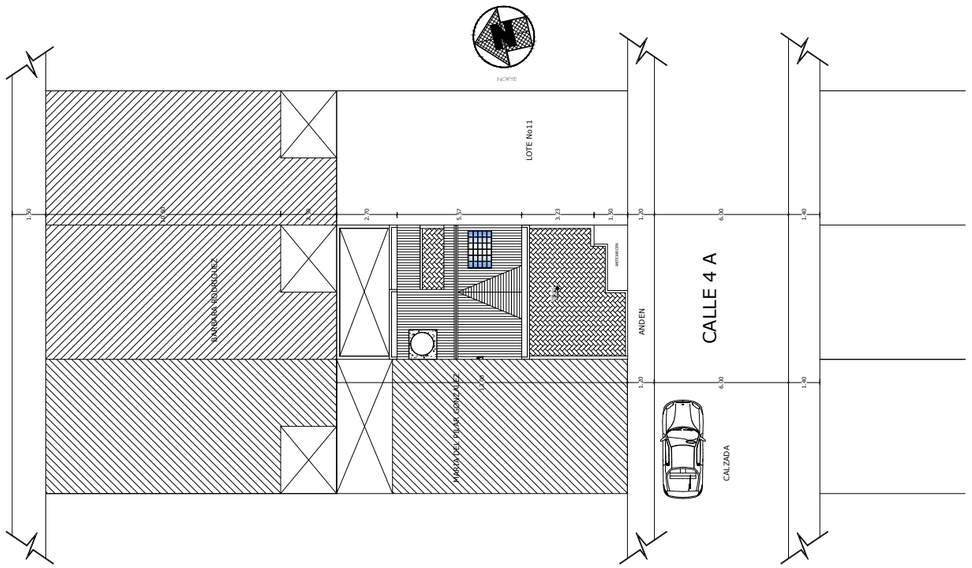

GENERAL LOCATION

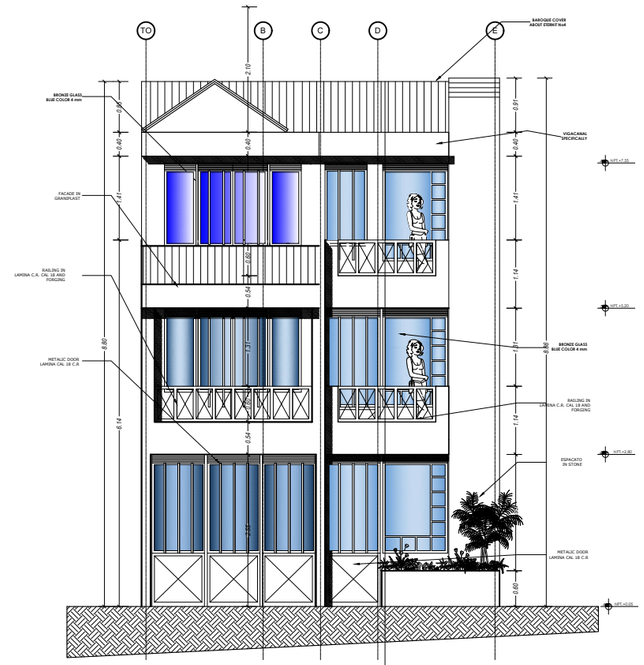

MAIN FACHADA

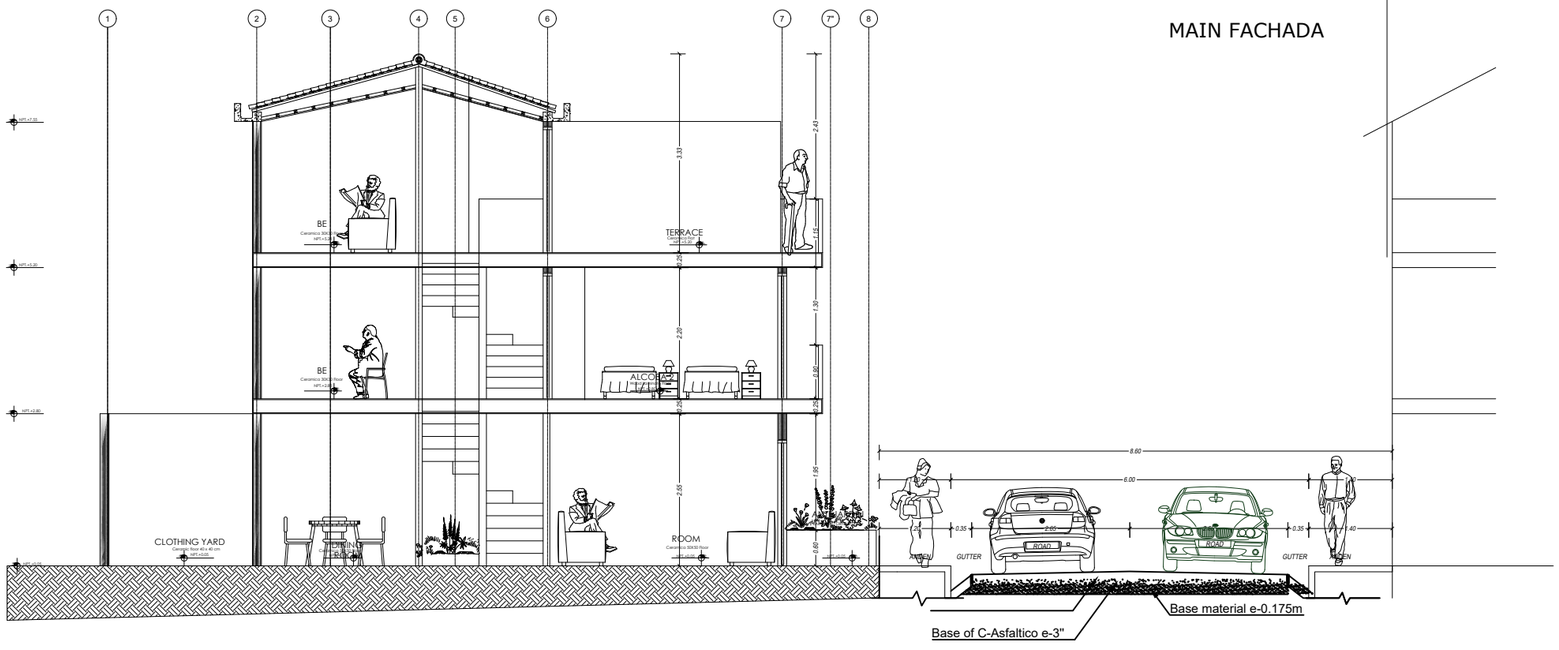

URBAN PROFILE

For more plans like these visit:

freecadfloorplans.com

Project name: sections

Drawing title: Architectural plans

CAD drawing: -

Scale 1:100

Sheet number 02

This plans are for educational or personal use only, it is illegal by copyright laws to use it for commercial purposes.

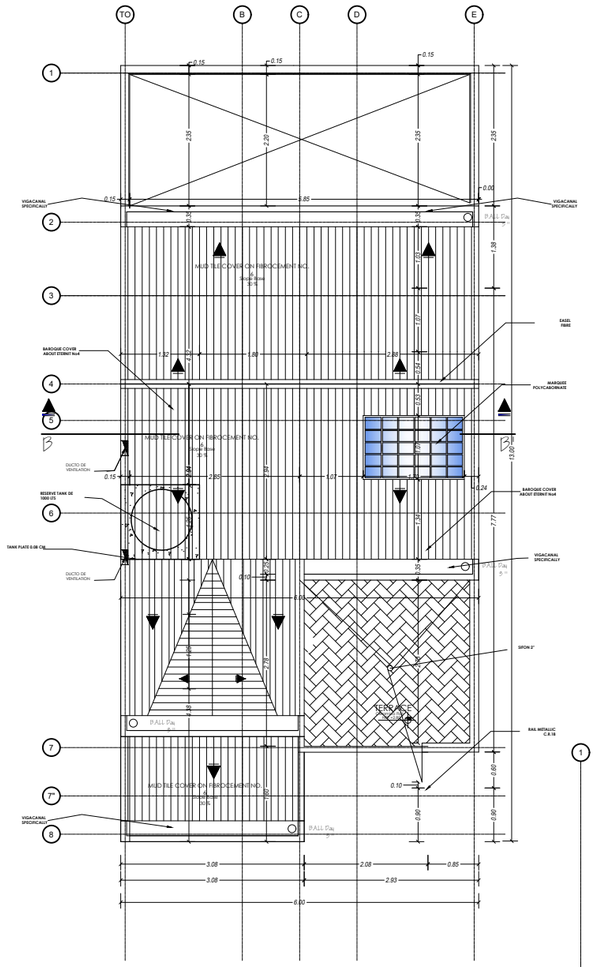

FLOOR COVERED

AREAS TABLE	
TOTAL LOT AREA	78.00 M^2
AREA BUILT FIRST FLOOR	54.68M^2
AREA BUILT SECOND FLOOR	58.32 M^2
AREA BUILT MEZZANINE	22.94 M^2
TOTAL AREA CONSTRUCTED	135.94 M^2
FREE AREA	19.70 M^2
CONSTRUCTION INDEX	1.74
OCCUPATION INDEX	0.70
AREA TO LICENSE	136.88 M^2

AREAS TABLE

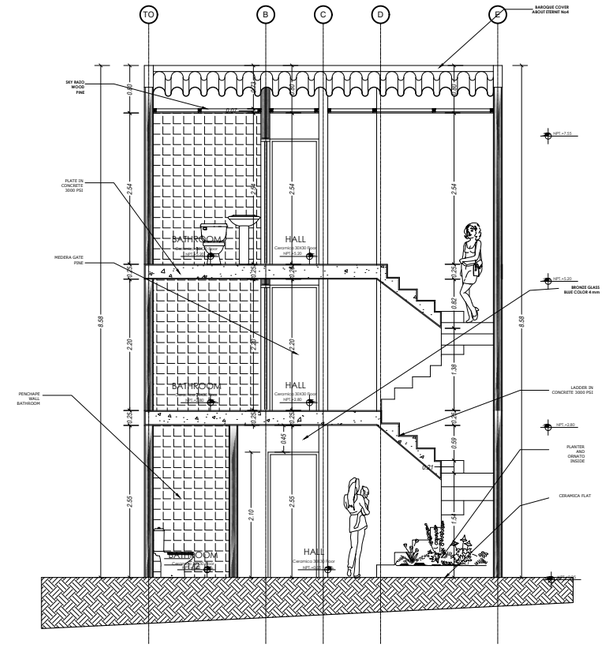

TRANSVERSAL COURT B___B"

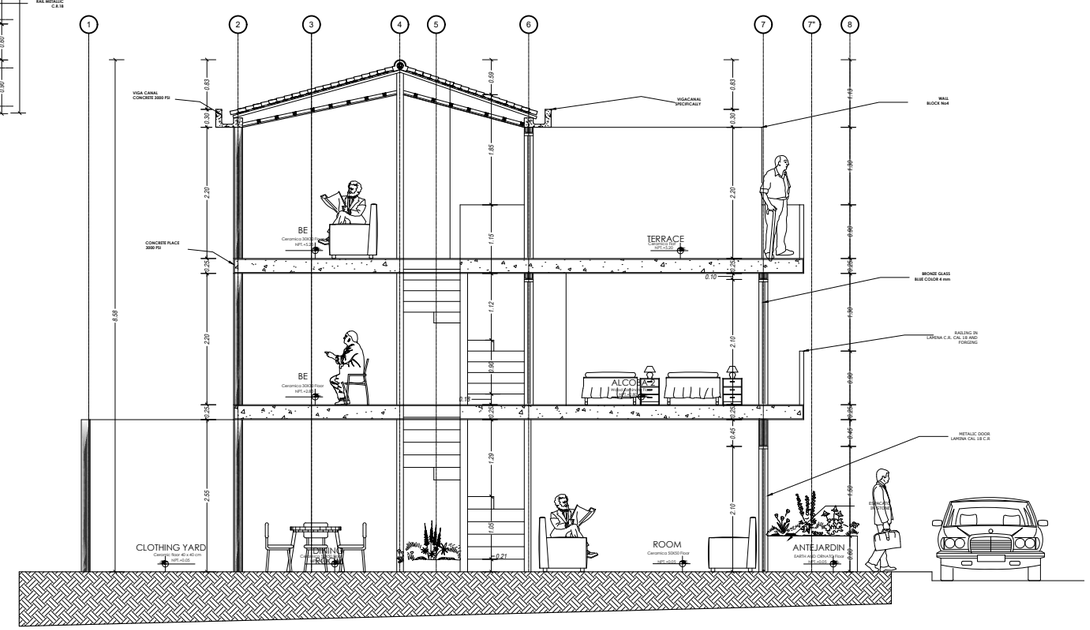

LONGITUDINAL CUTTING A__A"

For more plans like these visit:

freecadfloorplans.com

Project name:

20X40 house
4 bedroom

Drawing title:

elevations

CAD drawing:

-

Scale

1:100

Sheet number

03

This plans are for educational or personal use only, it is illegal by copyright laws to use it for commercial purposes.

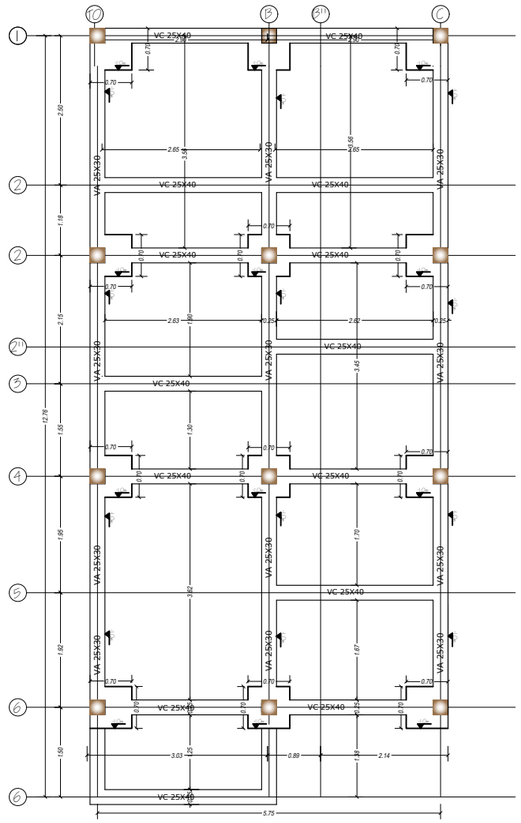

CIMENTACION PLANT

SCALE 1_____50

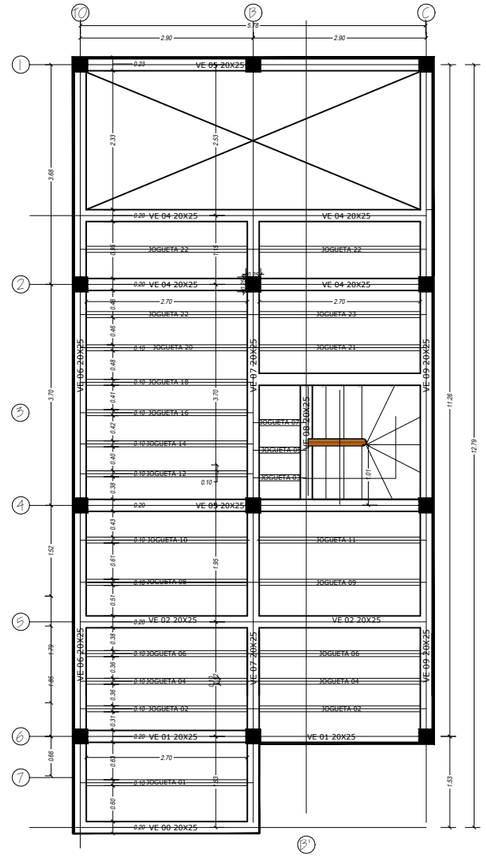

MEZZANINE PLANT 1

SCALE 1_____50

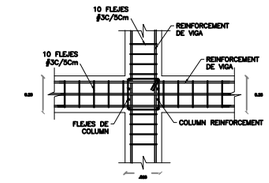

PLANT
COLUMA-VIGAS KNOT

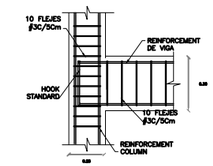

ELEVATION
COLUMA-VIGAS KNOT

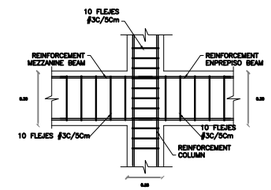

ELEVATION
COLUMA-VIGAS KNOT

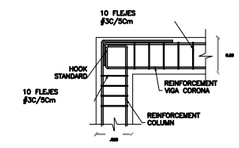

PLANT
ANCHORING THE LAST LEVEL

DETAILS RIGID ZONES

SCALE 1_____20

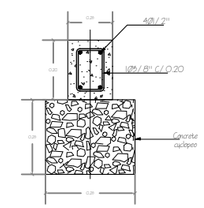

TYPICAL SECTION OF CIMENTACION VC
FOR COLUMNS C1

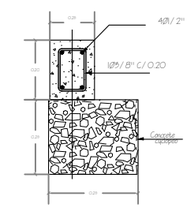

TYPICAL SECTION OF CIMENTACION VC
FOR COLUMNS C1

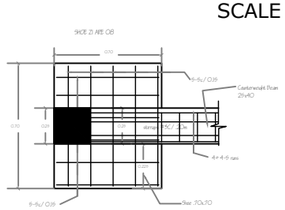

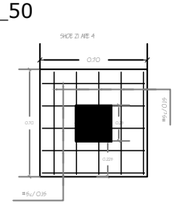

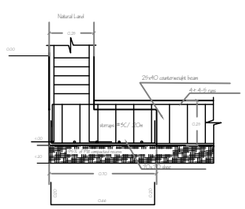

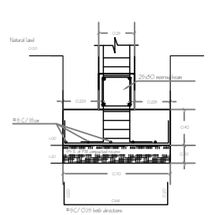

SHOE DETAILS

SCALE 1_____30

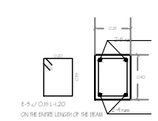

COUNTERWEIGHT BEAM SECTION

SCALE 1_____30

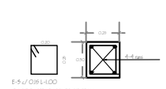

MOORING BEAM SECTION

SCALE 1_____30

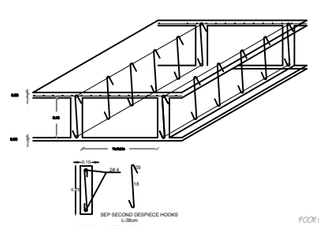

TIPIC CROSS-FLOOR PLATE CUTTING

NON-STOP

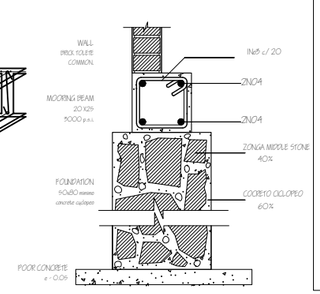

CIMENTACION DETAIL

SPECIFICATIONS

1- CONCRETE

F´c	Mpa	Kg / cm2	P.S.I.
-COLUMNS	21	210	3.000
-VIGAS AND PLATES	21	210	3.000
-CYCLOPEOS	17.5	175	2.500

2- STEELS

F´sud	Mpa	Kg / cm2
Ø 3/8"	420	2400
Ø > 3/8" (PERNOS)	420	4200
CERCHA, CONNECTIONS	560	5600

NOMENCLATURE RODS AND HOOK USED

NUMBER	2	3	4	5	6	7	8
DIAMETER INCHES		3/8	1/2	5/8	3/4	7/8	1
LONG GANCHO Cm	10	15	20	25	30	35	40

3- LIVING DESIGN LOAD

	Kg / m2
FLOOR PLATES	180
WALLS	200
COVER	50

4- NOTES

4.1.- ANY MODIFICATION MUST BE APPROVED BY THE CALCULIST

4.2.- THE SIZING AND DESIGN OF THE STRUCTURAL ELEMENTS - BEAMS , JOISTS AND COLUMNS) IT WAS PREPARED ON THE DESIGN ARCHITECTS.

4.3.- THE FILLERS MAY NOT VARY OR LOCATE OF DIMENSIONS OF THE STRUCTURAL ELEMENTS

4.4.- THE STRUCTURE CANNOT BE OVERLOADED WITH NON-CHANGED PLANNED IN THE DESIGN

4.5.- THE FILLERS MUST STRICTLY VERIFY THE COORDINATION OF THE STRUCTURAL PLANS WITH THE ARCHITECTURAL PLANS AND FACILITIES

4.6.- THE MINIMUM COVERING OF STRUCTURAL ELEMENTS IS 4Cm

4.7.- CONCRETE SAMPLES MUST BE TAKEN TO VERIFY THE RESISTANCE OF THE ELEMENTS THAT ARE POURED

4.8.- THE TRUSS FILLE MUST BE PLACED TO MINIMUM 5Cm OF THE FACE OF THE BEAM OR COLUMN AS APPROPRIATE

For more plans like these visit:

freecadfloorplans.com

Project name:

20X40 house
4 bedroom

Drawing title:

structural

CAD drawing:

-

Scale

1:100

Sheet number

04

This plans are for educational or personal use only, it is illegal by copyright laws to use it for commercial purposes.